



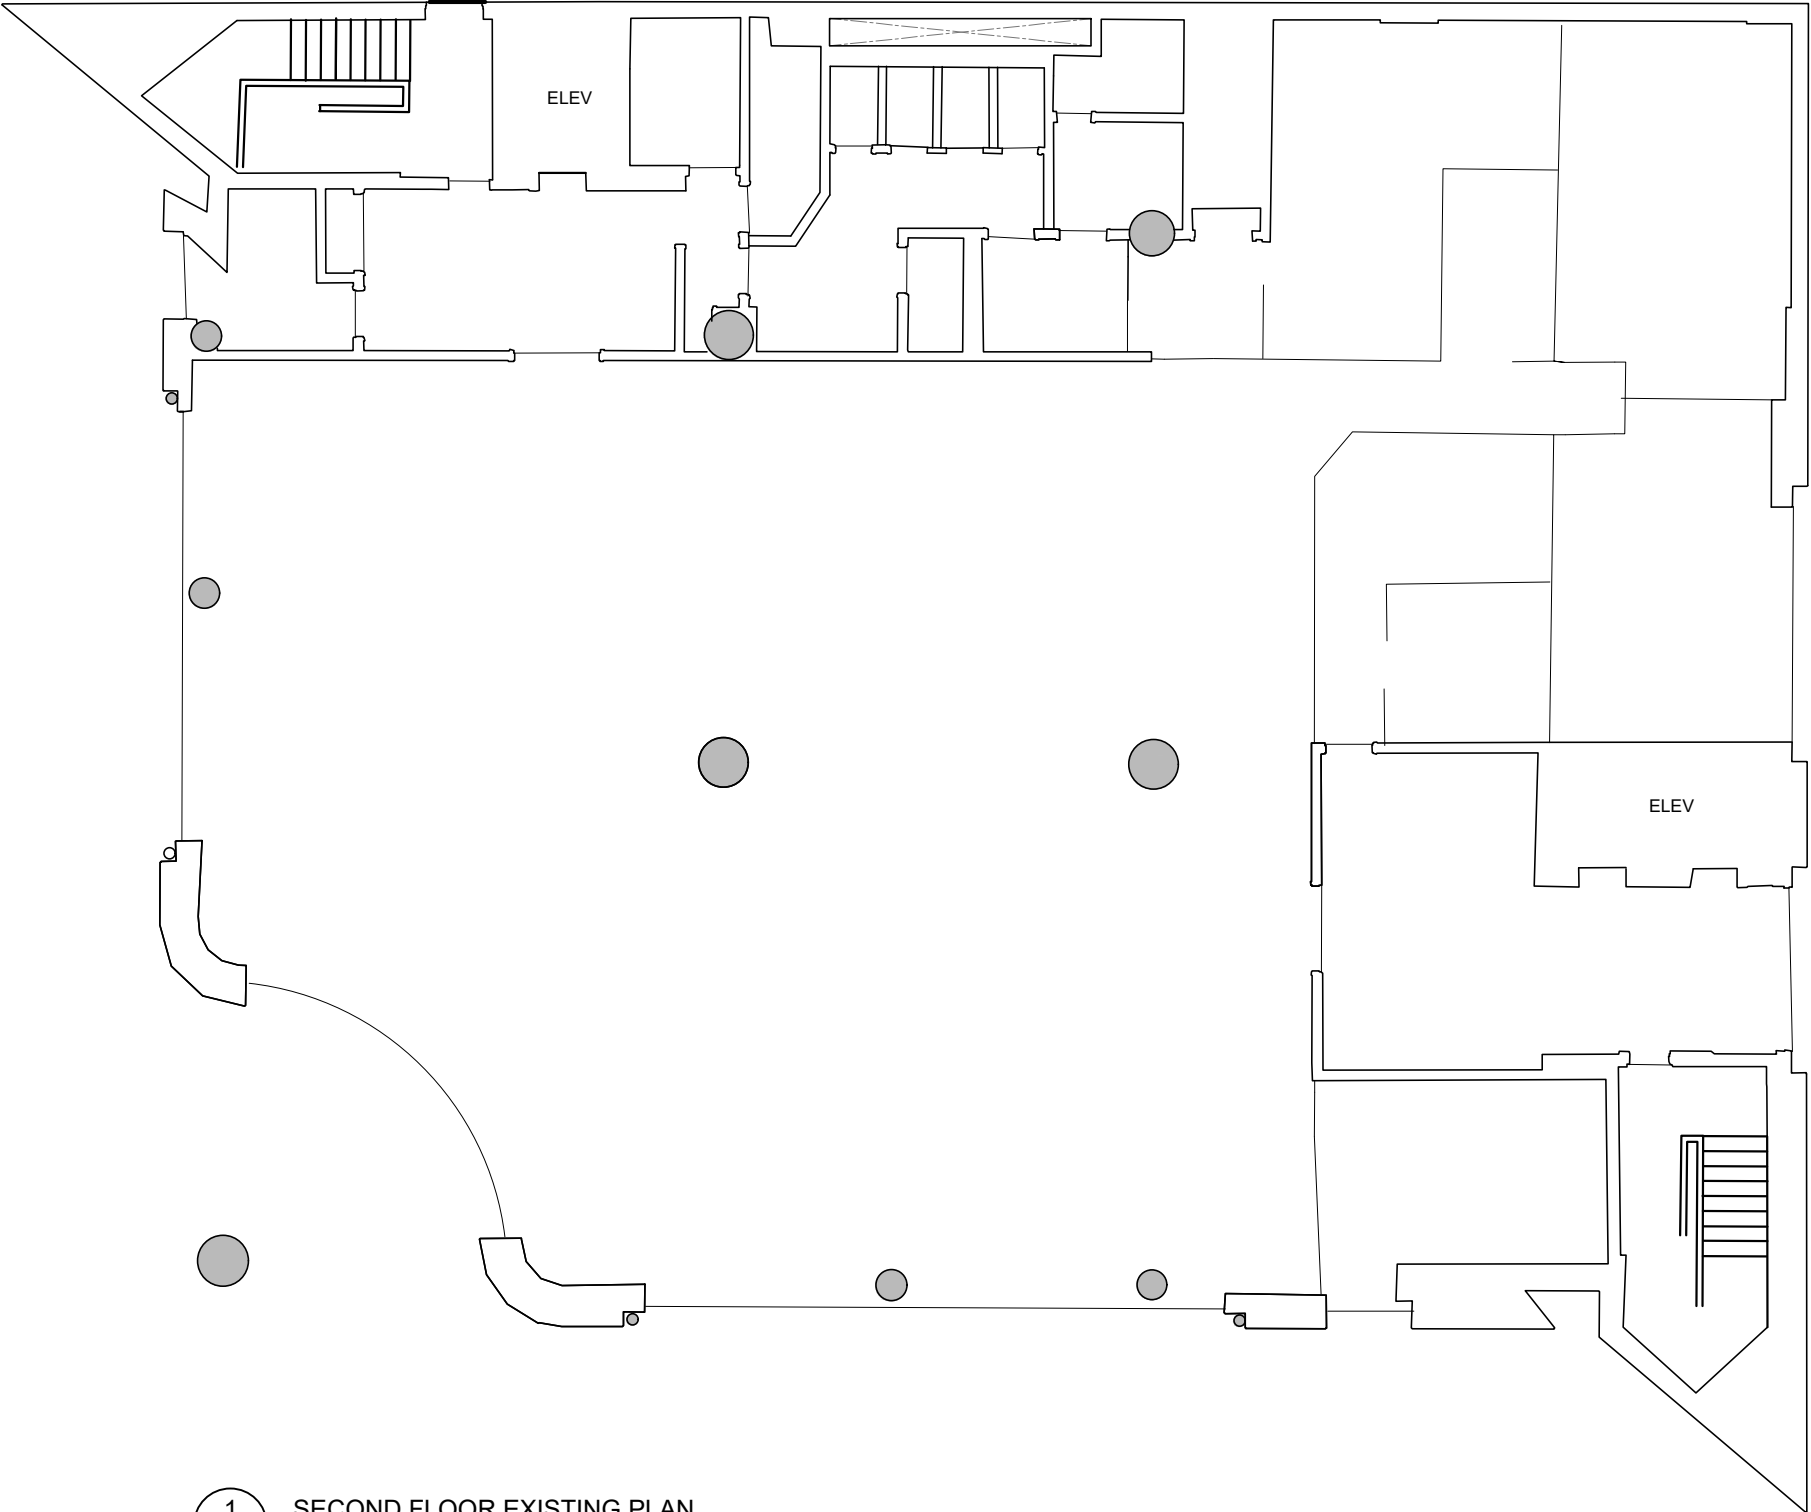


1 SECOND FLOOR EXISTING PLAN
I-008c SCALE 1:150

key concept (407A) BLDG. 4, DUBAI DESIGN DISTRICT, DUBAI, UNITED ARAB EMIRATES	CONSULTANT	OWNER	PROJECT TITLE	NO.	DESCRIPTION	DATE	SHEET TITLE :	SHEET NO.
			AL HABIB PAVILION HQ	01	TENDER UPDATE	2023.03.22	SECOND FLOOR EXISTING PLAN	I-008c
				02	TENDER UPDATE	2023.04.06	SCALE 1:150	
				03	TENDER UPDATE	2023.04.12	DATE: 2023.03.03	
				04	MEETING ROOM CABINET UPDATE	2023.04.25	APPROVED BY: AN DRAWN BY: AN	
		ADDRESS: JEDDAH, KSA		04a	TENDER UPDATE	2023.05.05	DESIGNED BY: AN CHECKED BY: AN	

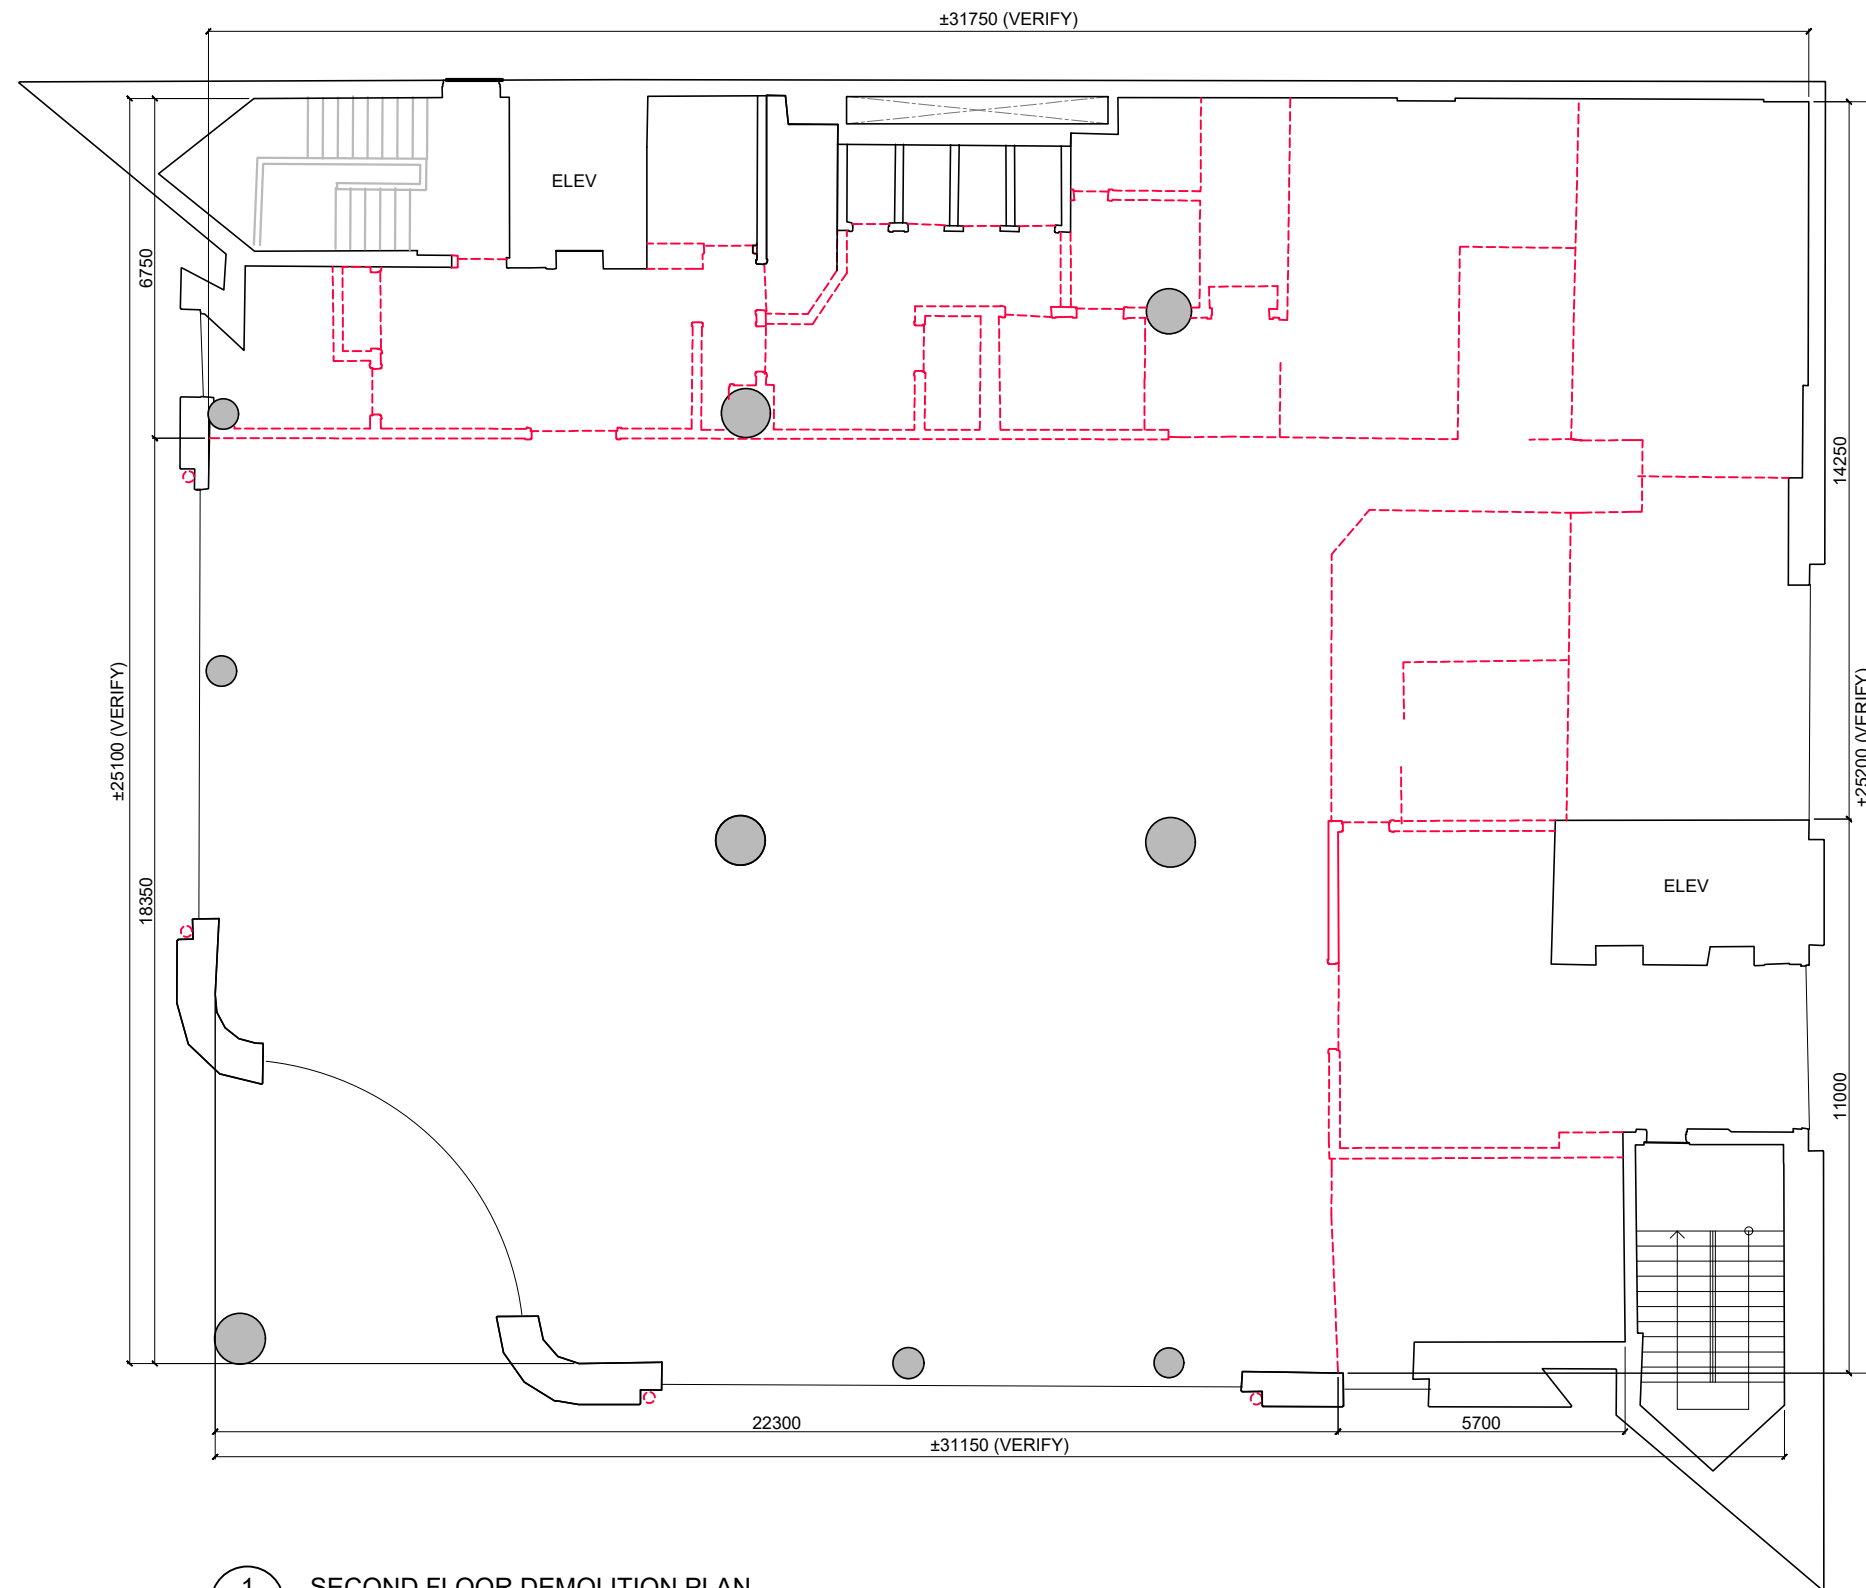

1 SECOND FLOOR DEMOLITION PLAN
I-009b SCALE 1:150

key concept (407A) BLDG. 4, DUBAI DESIGN DISTRICT, DUBAI, UNITED ARAB EMIRATES	CONSULTANT	OWNER	PROJECT TITLE	NO.	DESCRIPTION	DATE	SHEET TITLE :	SHEET NO.
			AL HABIB PAVILION HQ	01	TENDER UPDATE	2023.03.22	SECOND FLOOR DEMOLITION PLAN	I-009b
				02	TENDER UPDATE	2023.04.06	SCALE 1:150	
				03	TENDER UPDATE	2023.04.12	DATE: 2023.03.03	
				04	MEETING ROOM CABINET UPDATE	2023.04.25	APPROVED BY: AN DRAWN BY: AN	
		ADDRESS: JEDDAH, KSA		04a	TENDER UPDATE	2023.05.05	DESIGNED BY: AN CHECKED BY: AN	

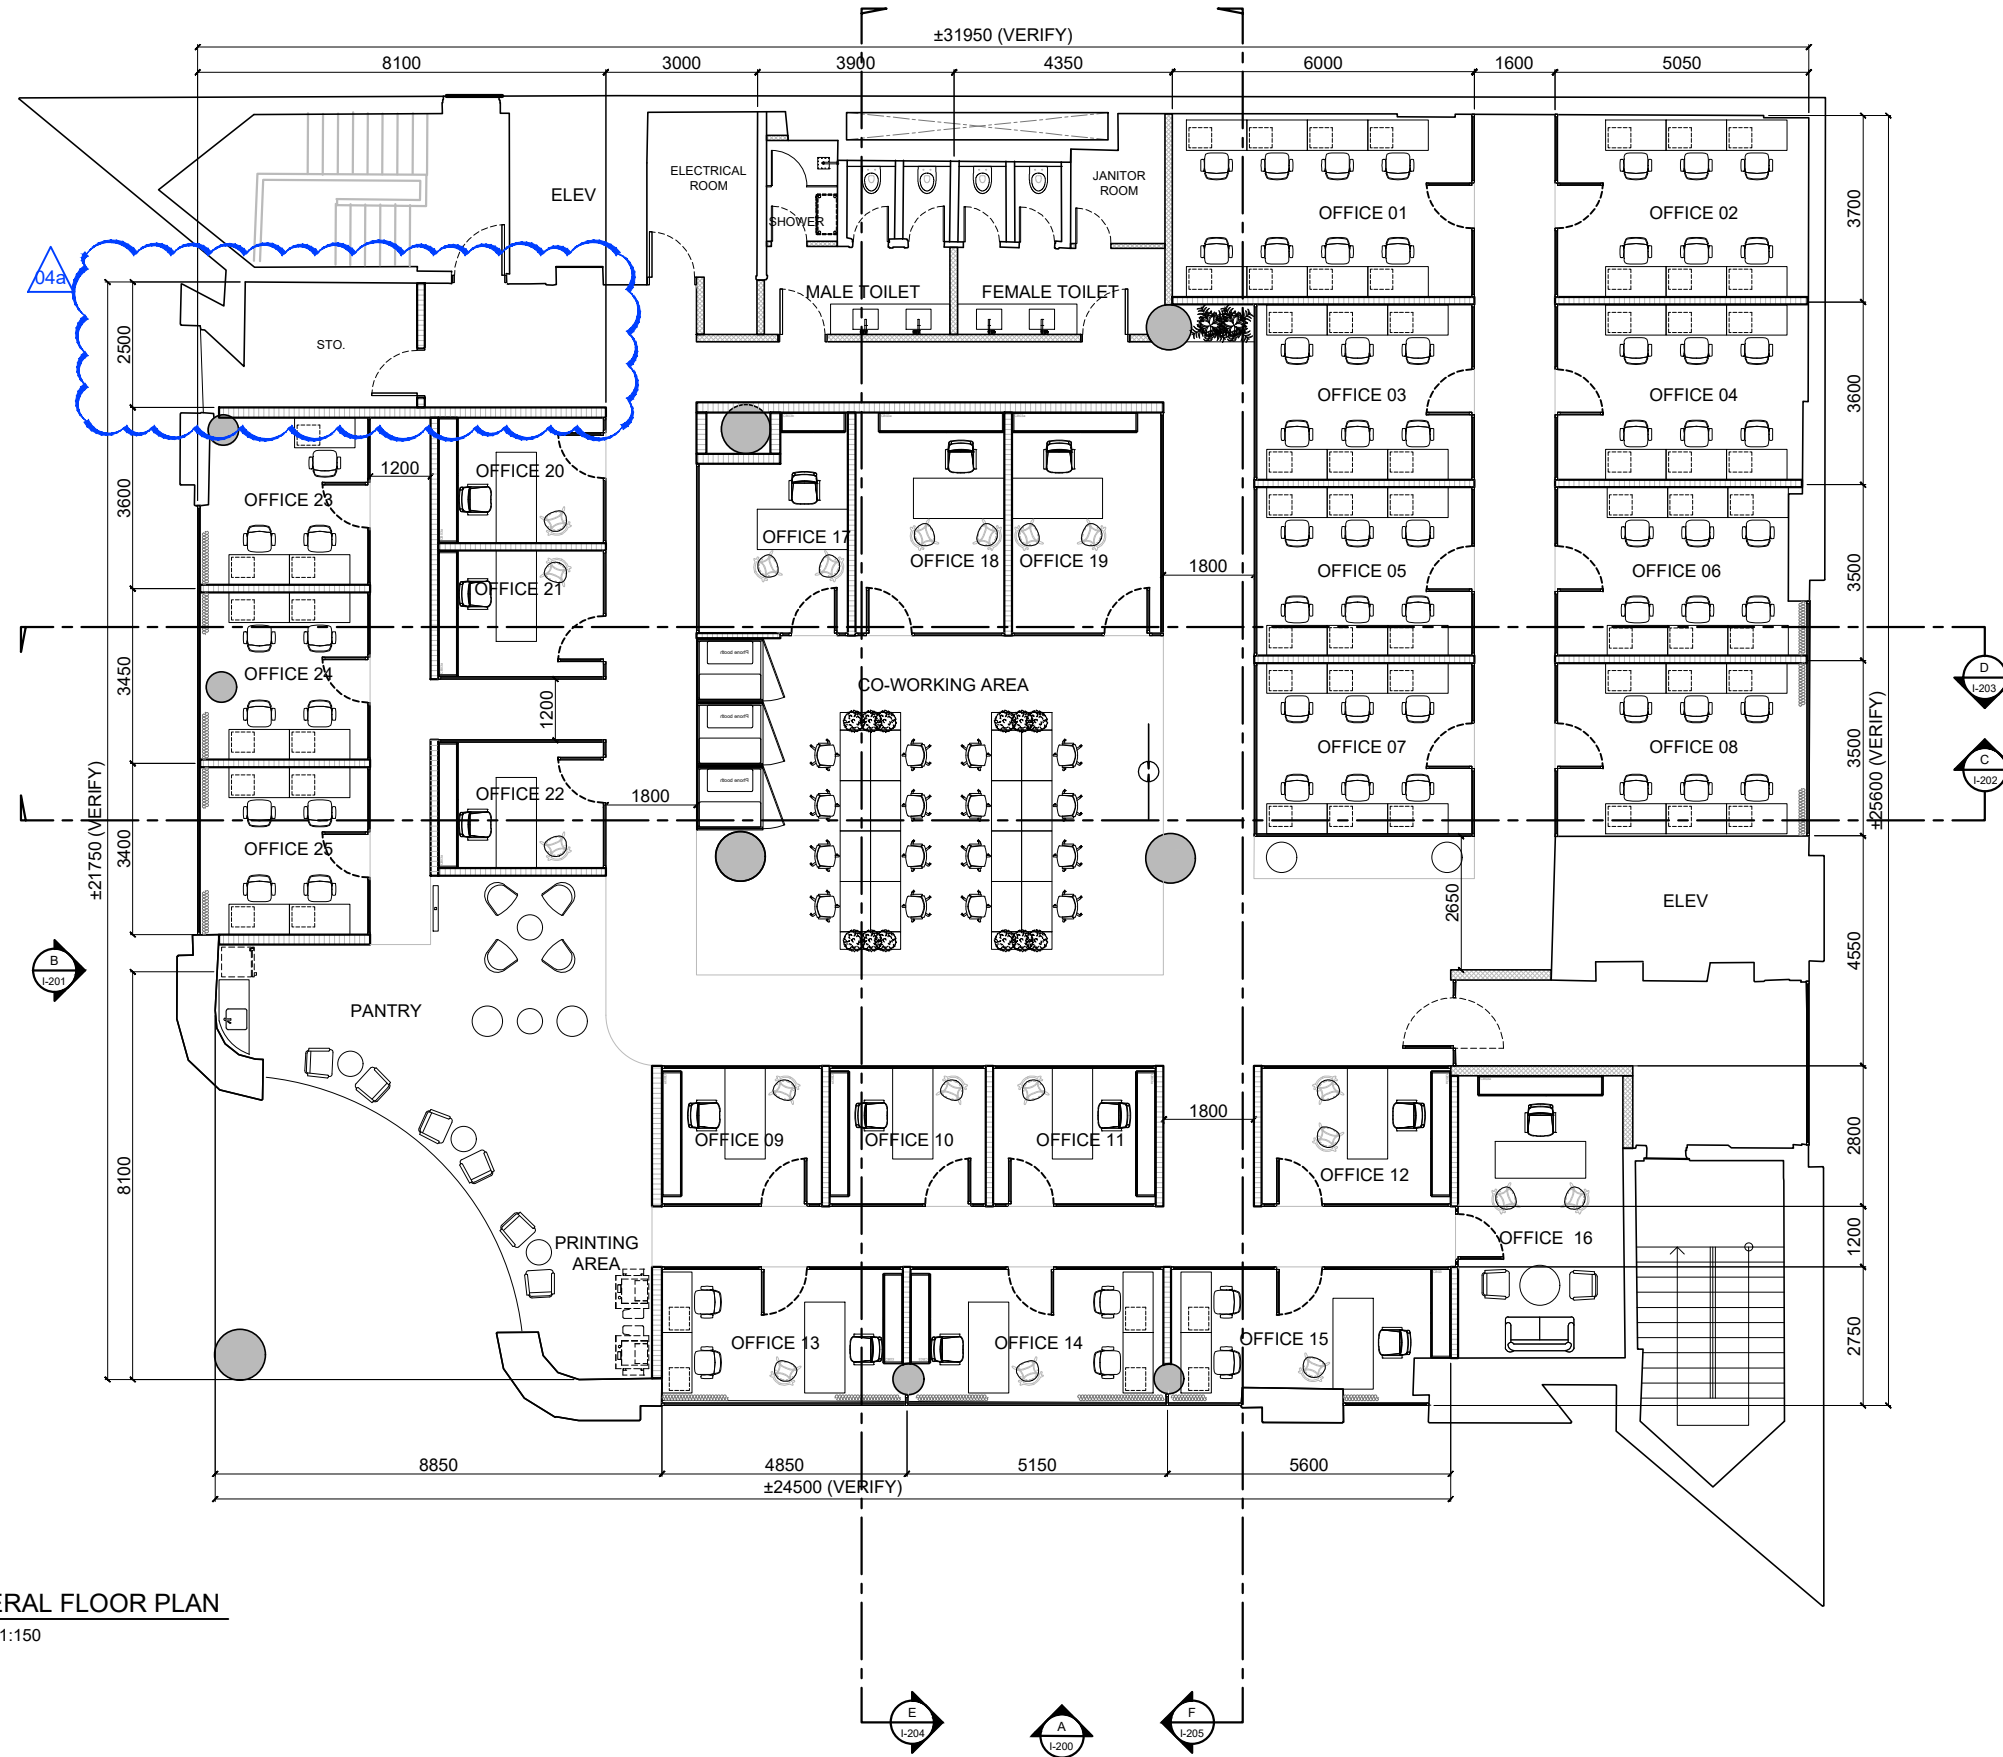


1 SECOND GENERAL FLOOR PLAN
I-100b SCALE 1:150

key
concept

(407A) BLDG. 4, DUBAI DESIGN DISTRICT, DUBAI, UNITED ARAB EMIRATES

CONSULTANT	OWNER	PROJECT TITLE	NO.	DESCRIPTION	DATE	SHEET TITLE :	SHEET NO.
		AL HABIB PAVILION HQ	01	TENDER UPDATE	2023.03.22	SECOND GENERAL FLOOR PLAN	I-100b
			02	TENDER UPDATE	2023.04.06	SCALE 1:150	
			03	TENDER UPDATE	2023.04.12	DATE: 2023.03.03	
			04	MEETING ROOM CABINET UPDATE	2023.04.25	APPROVED BY: AN DRAWN BY: AN	
			04a	TENDER UPDATE	2023.05.05	DESIGNED BY: AN CHECKED BY: AN	
	ADDRESS: JEDDAH, KSA						

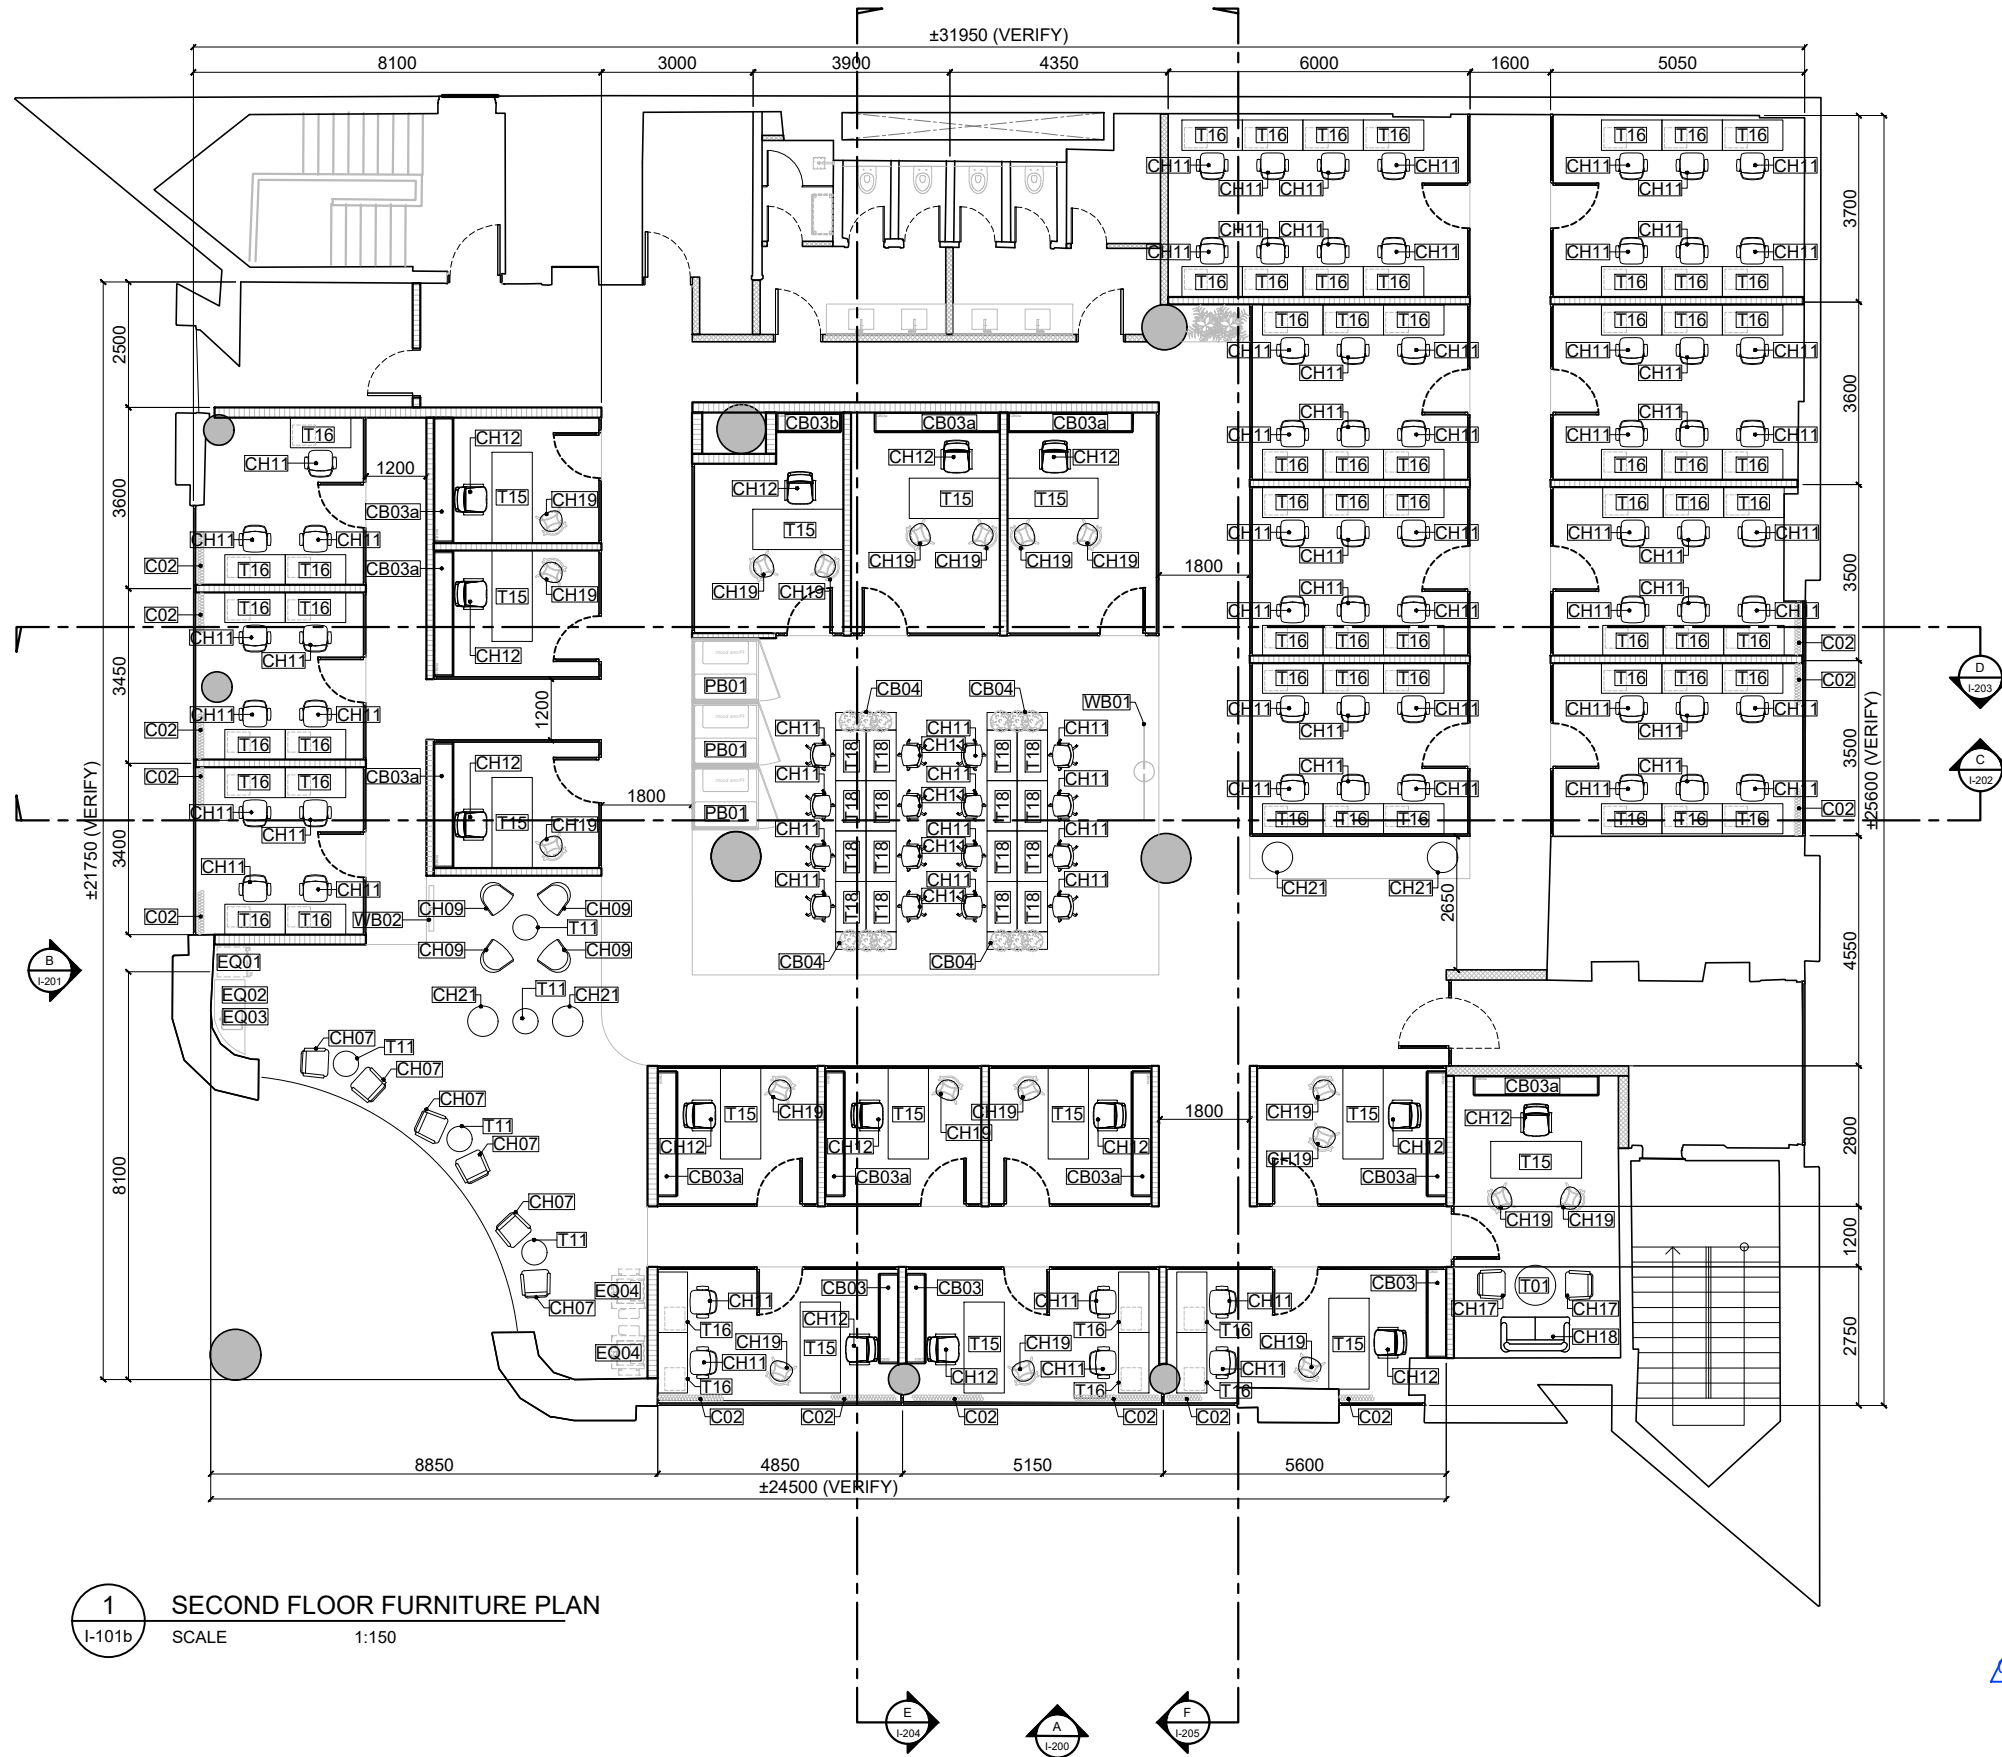


1 SECOND FLOOR FURNITURE PLAN
I-101b SCALE 1:150

LEGENDS:			LEGENDS:		
CHAIRS			TABLES		
CH01	RECEPTION CHAIR		T01	800mm dia ROUND COFFEE TABLE	
CH02	LOUNGE CHAIR A		T02	700x700mm DINNING TABLE	
CH02a	LOUNGE CHAIR A		T03	700x1050mm DINNING TABLE	
CH03	LOUNGE CHAIR B		T03a	700x1500mm DINNING TABLE	
CH03a	LOUNGE CHAIR B		T04	900x1600mm MEETING TABLE	
CH04	DINNING CHAIR A		T05	900x2400mm MEETING TABLE	
CH05	OTTOMAN		T06	1000x4000mm MEETING TABLE	
CH06	MEETING CHAIR		T07	900mm dia ROUND MEETING TABLE	
CH07	LOUNGE CHAIR C		T08	800mm dia ROUND COFFEE TABLE	
CH08	BEAN BAG		T09	450mm dia ROUND COFFEE TABLE	
CH09	LOUNGE CHAIR D		T10	800mm dia ROUND COFFEE TABLE	
CH10	BAR COUNTER CHAIR		T11	450mm dia ROUND COFFEE TABLE	
CH11	WORKSTATION CHAIR		T12	800mm dia ROUND COFFEE TABLE	
CH12	EXECUTIVE CHAIR		T13	800x800mm OUTDOOR DINING TABLE	
CH13	OFICE CHAIR		T14	325x600mm SIDE TABLE	
CH14	LOUNGE CHAIR E		T15	800x1800mm EXECUTIVE TABLE	
CH15	LOUNGE CHAIR F		T16	700x1400mm WORKSTATION TABLE	
CH16	LOUNGE CHAIR G		T17	600x1000mm EXECUTIVE TABLE	
CH17	LOUNGE CHAIR H		T18	600x1000mm WORKSTATION TABLE	
CH18	LOUNGE CHAIR I		T19	OVAL-SHAPED OUTDOOR COFFEE TABLE	
CH19	GUEST CHAIR		T20	700x1800mm OFFICE TABLE	
CH20	LOUNGE CHAIR J		T21	4800x1000mm MEETING TABLE	
CH21	600 mm dia ROUND POUFS		T22	750mm dia ROUND DINNING TABLE	
CH22	OUTDOOR DINING CHAIR		T23	800mm dia TABLE	
CH23	DINNING CHAIR B		T24	2500x600mm COUNTER	
CH24	LOUNGE CHAIR K		T25	800x3000mm RECEPTION COUNTER	
CH25	LOUNGE CHAIR L		T26	800x3000mm RECEPTION COUNTER	
CH26	OUTDOOR 2-SEATER LOUNGE SOFA		T27	450mm dia ROUND SIDE TABLE	
CH27	OUTDOOR CURVED LOUNGE SOFA		PB01	PHONE BOOTH	
CH28	OUTDOOR BEAN BAG		LB01	LIBRARY BOX	
			CB01	400x2600mm LOW CABINET	
			CB01a	400x1500mm LOW CABINET	
			CB02	400x2600mm WALL CABINET	
			CB03	400x1800mm WALL CABINET	
			CB03a	400x2500mm WALL CABINET	
			CB03b	400x1300mm WALL CABINET	
			CB03c	400x3000mm WALL CABINET	
			CB04	350x1200mm LOW CABINET W/ PLANTBOX	
			DS01	DISPLAY SHELVE	
			BD01	SINGLE SIZE BED	
			P01	1500x1900mm BUILT-IN PLANTERBOX	
			P02	1200x2800mm BUILT-IN PLANTERBOX	
			P03	500x1140mm BUILT-IN PLANTERBOX	
			P04	500x800mm BUILT-IN PLANTERBOX	
			P05	600x600mm BUILT-IN PLANTERBOX	
			BS01	BUILT-IN SEATING A	
			BS02	BUILT-IN SEATING B	
			LC01	LIBRARY CABINET	
			EQ01	REFRIGERATOR	
			EQ02	MICROWAVE	
			EQ03	OVEN	
			EQ04	PRINTER	
			DS01	DIGITAL SCREEN	
			SC01	WALL MOUNTED 65" TV SCREEN	
			SC02	TABLETOP 65" TV SCREEN	
			WS01	WALL SCULPTURE	

key concept		CONSULTANT	OWNER	PROJECT TITLE	NO.	DESCRIPTION	DATE	SHEET TITLE :		SHEET NO.
				AL HABIB PAVILION HQ	01	TENDER UPDATE	2023.03.22	SECOND FLOOR FURNITURE PLAN		I-101b
					02	TENDER UPDATE	2023.04.06	SCALE 1:150		
					03	TENDER UPDATE	2023.04.12	DATE: 2023.03.03		
					04	MEETING ROOM CABINET UPDATE	2023.04.25	APPROVED BY: AN DRAWN BY: AN		
(407A) BLDG. 4, DUBAI DESIGN DISTRICT, DUBAI, UNITED ARAB EMIRATES			ADDRESS: JEDDAH, KSA		04a	TENDER UPDATE	2023.05.05	DESIGNED BY: AN	CHECKED BY: AN	


LEGENDS:	
WALL FINISH	
WF01	"BEIGE" TEXTURED PAINT FINISH
WF02	TRAVERTINE CLADDING
WF03	"DARK OAK" WOOD LAMINATE FINISH
WF04	VERTICAL WOOD PANEL IN "LIGHT OAK" LAMINATE FINISH
WF05	600x1200mm "BEIGE" CERAMIC WALL TILE
WF06	DARK WOOD LAMINATE CLADDING
WF07	VERTICAL FLUTED WOOD
WF08	"LIGHT OAK" WOOD LAMINATE FINISH
WF09	"WHITE WRITABLE" PAINT FINISH
WF10	"BRONZE" POWDER COATED FINISH
WF11	PADDED WALL IN "TERRACOTTA" FABRIC FINISH
FLOOR FINISH	
FF01	TRAVERTINE FLOOR FINISH
FF02	MARBLE FLOOR FINISH
FF03	200mm HIGH RAISED FLOORING IN "LIGHT OAK" LAMINATE WOOD FLOOR
FF04	PATTERNED CARPET FLOOR FINISH
FF05	600x600mm "BEIGE" CERAMIC FLOOR TILE
FF06	WOOD FLOOR FINISH
FF07	BEIGE TERRAZZO TILES FLOOR FINISH
FF08	SAUDI BIANCO FLOOR FINISH
FF09	"BEIGE" EPOXY FLOOR FINISH
FLOOR AND WALL FIXTURES	
	L01 - TABLE LAMP A
	L01a - TABLE LAMP B
	L02 - FLOOR LAMP
	L03 - WALL LAMP
	L17 - PLANT LIGHT
	L19 - WALL MOUNTED LIGHT
	EQ05 - WALL MOUNTED PROJECTOR

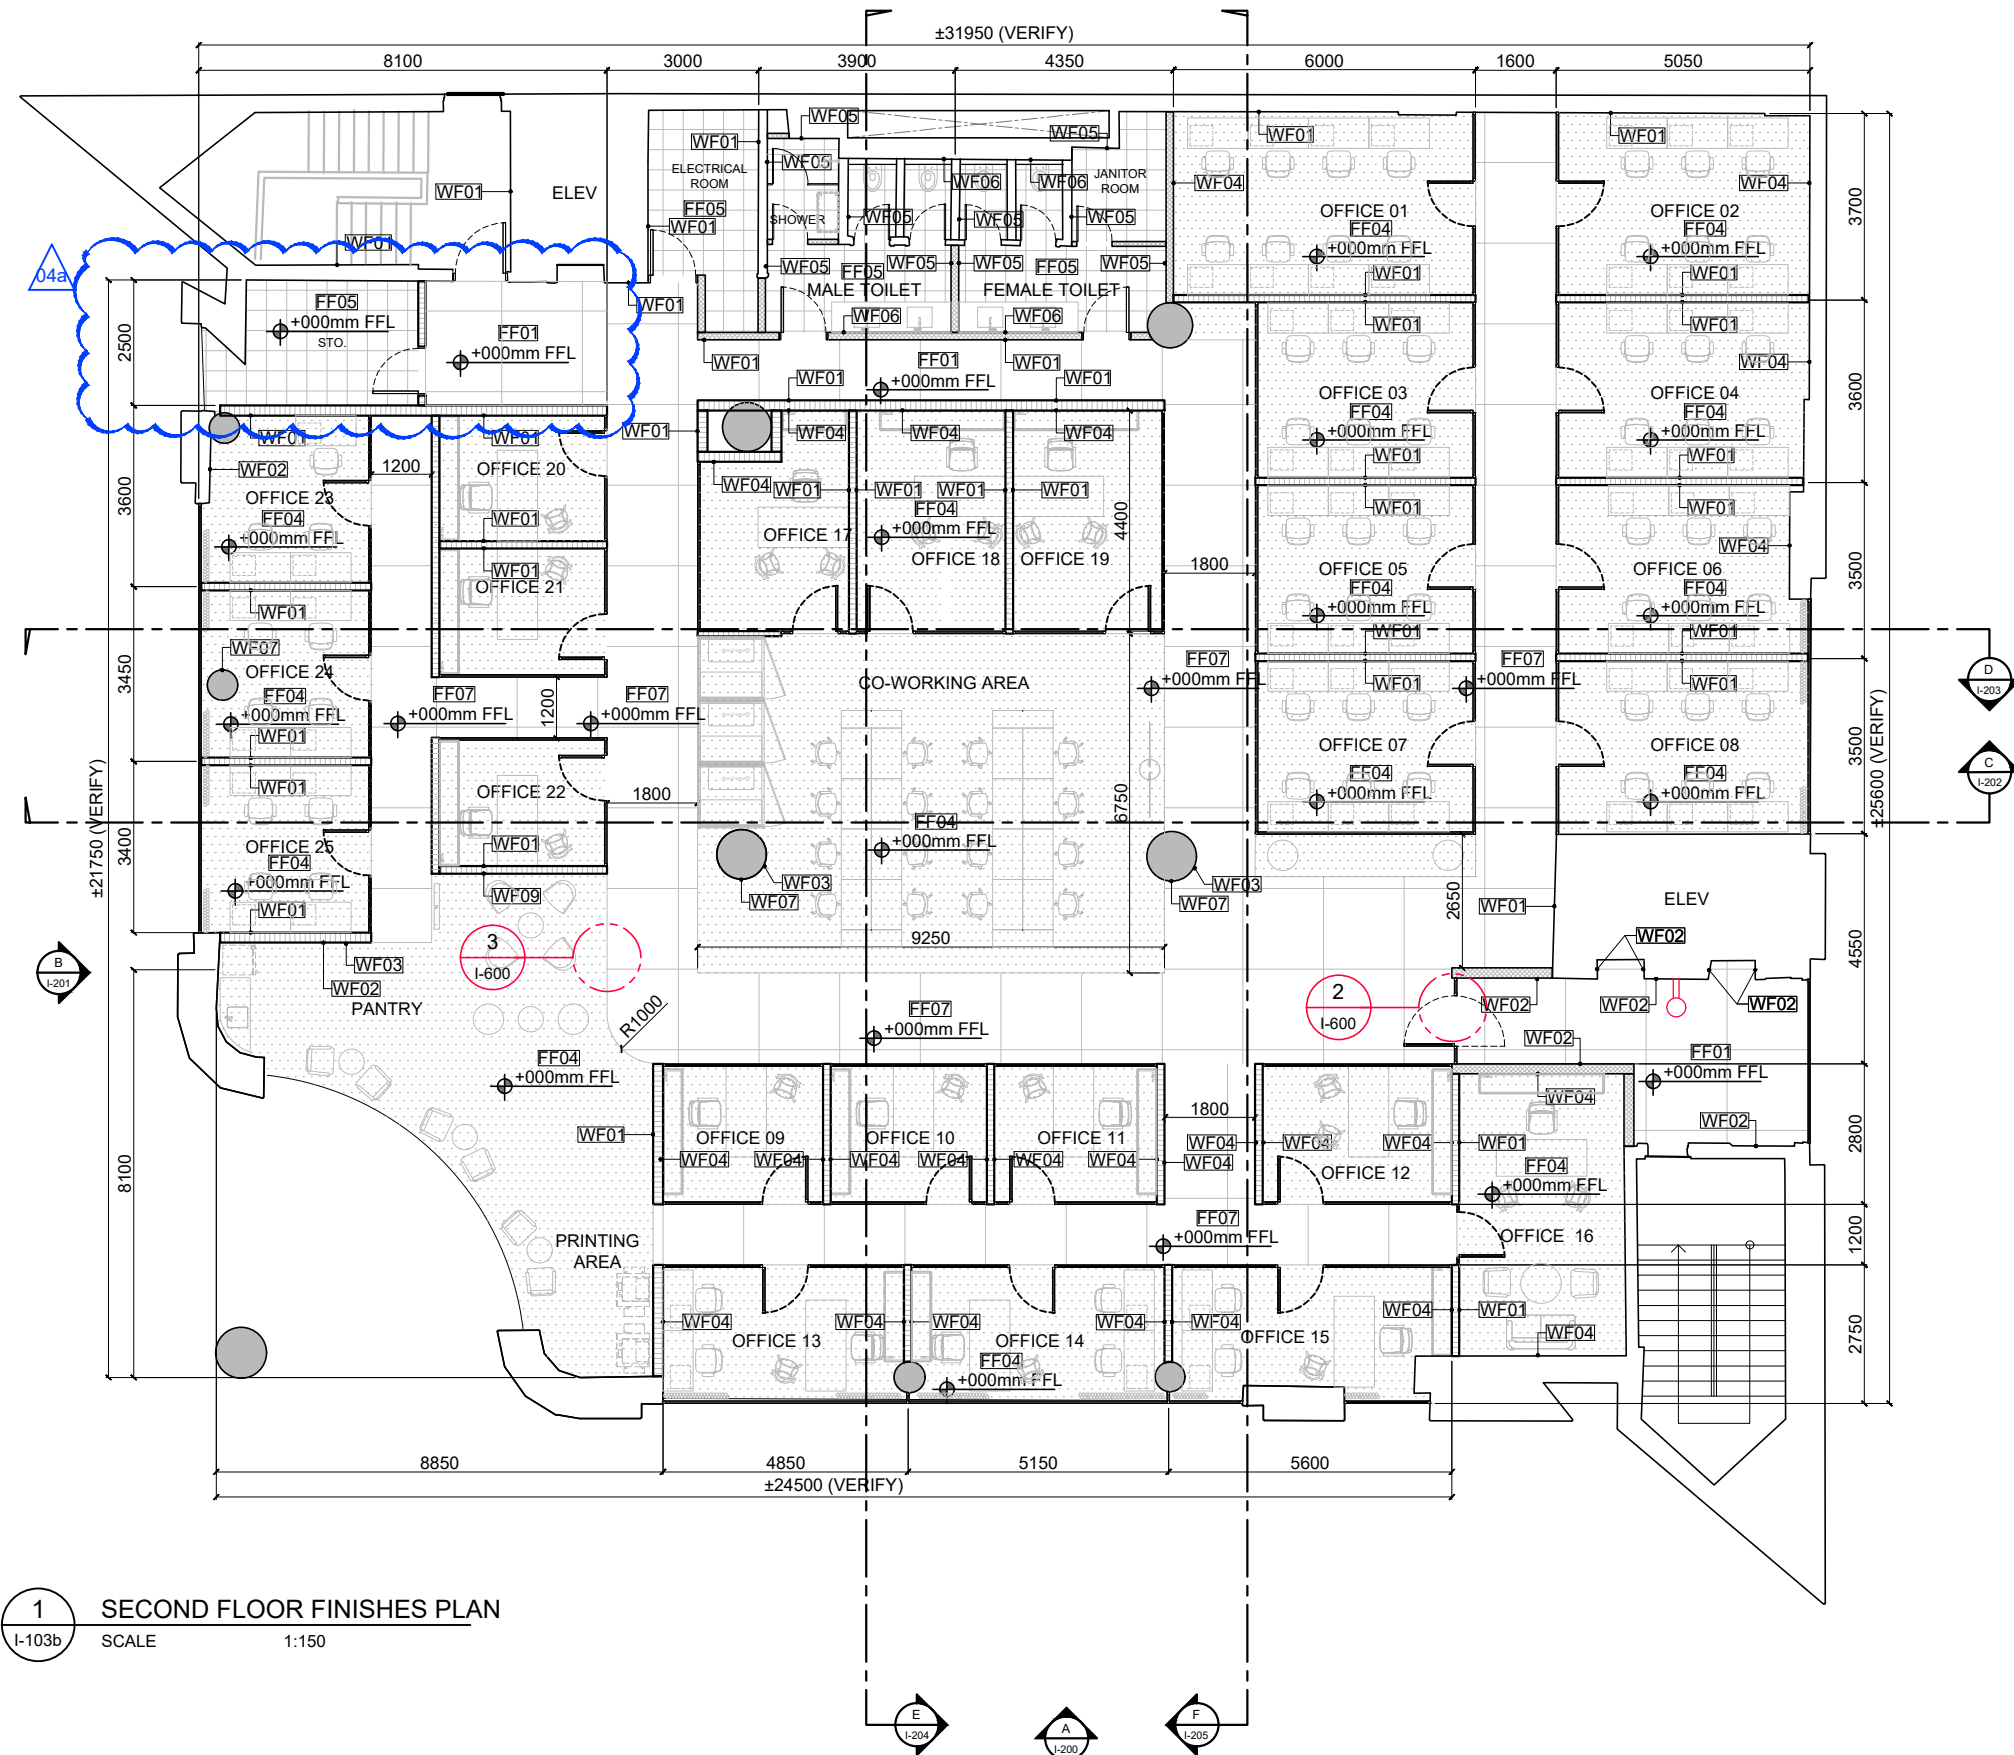

1 SECOND FLOOR FINISHES PLAN
I-103b SCALE 1:150

key concept		CONSULTANT	OWNER	PROJECT TITLE	NO.	DESCRIPTION	DATE	SHEET TITLE :		SHEET NO.
				AL HABIB PAVILION HQ	01	TENDER UPDATE	2023.03.22	SECOND FLOOR FINISHES PLAN		I-103b
					02	TENDER UPDATE	2023.04.06	SCALE 1:150		
					03	TENDER UPDATE	2023.04.12	DATE: 2023.03.03		
					04	MEETING ROOM CABINET UPDATE	2023.04.25	APPROVED BY: AN DRAWN BY: AN		
(407A) BLDG. 4, DUBAI DESIGN DISTRICT, DUBAI, UNITED ARAB EMIRATES			ADDRESS: JEDDAH, KSA		04a	TENDER UPDATE	2023.05.05	DESIGNED BY: AN CHECKED BY: AN		


LEGENDS:	
CEILING FINISHES	
CF01	12mm THK GYPSUM BOARD IN "BEIGE" PAINT TEXTURED FINISH general ceiling
CF02	12mm THK GYPSUM BOARD IN "CREAMY WHITE" PAINT FINISH toilets
CF03	EXPOSED CEILING WITH MEP ELEMENTS IN "BEIGE" PAINT FINISH circulation
CF04	12mm THK GYPSUM BOARD IN "CREAMY WHITE" PAINT FINISH ff reception
CF05	12mm THK MDF BOARD IN PATTERNED CARPET FINISH cultural majlis
CF06	"BRONZE" POWDER COATED FINISH CANOPY canopy
CEILING FIXTURES	
	L4- RECESSED ROUND LED DOWNLIGHT general light + offices
	L5- SUSPENDED ROUND LIGHT meeting room
	L6- RECESSED ROUND LED DOWNLIGHT toilets
	L7- PENDANT LIGHT A bar
	L8 - PENDANT LIGHT B waiting area
	L9- LED STRIPLIGHT meeting room
	L10 - SUSPENDED TASK LIGHT offices and co-working spaces
	L11 - RECESSED LINEAR LIGHT hallway
	L12 - SUSPENDED DOWNLIGHT general light
	L13 - CUSTOMIZED STRETCHED LIGHT vip gallery area
	L14 - CHANDELIER A cultural majlis area
	L15 - CHANDELIER B canopy
	L16 - PENDANT LIGHT C reception
	L18 - DECORATIVE BULB LIGHT facade
	CEILING MOUNTED SPEAKER
	RELOCATED SMOKE DETECTOR
	CCTV
	EMERGENCY EXIT LIGHT

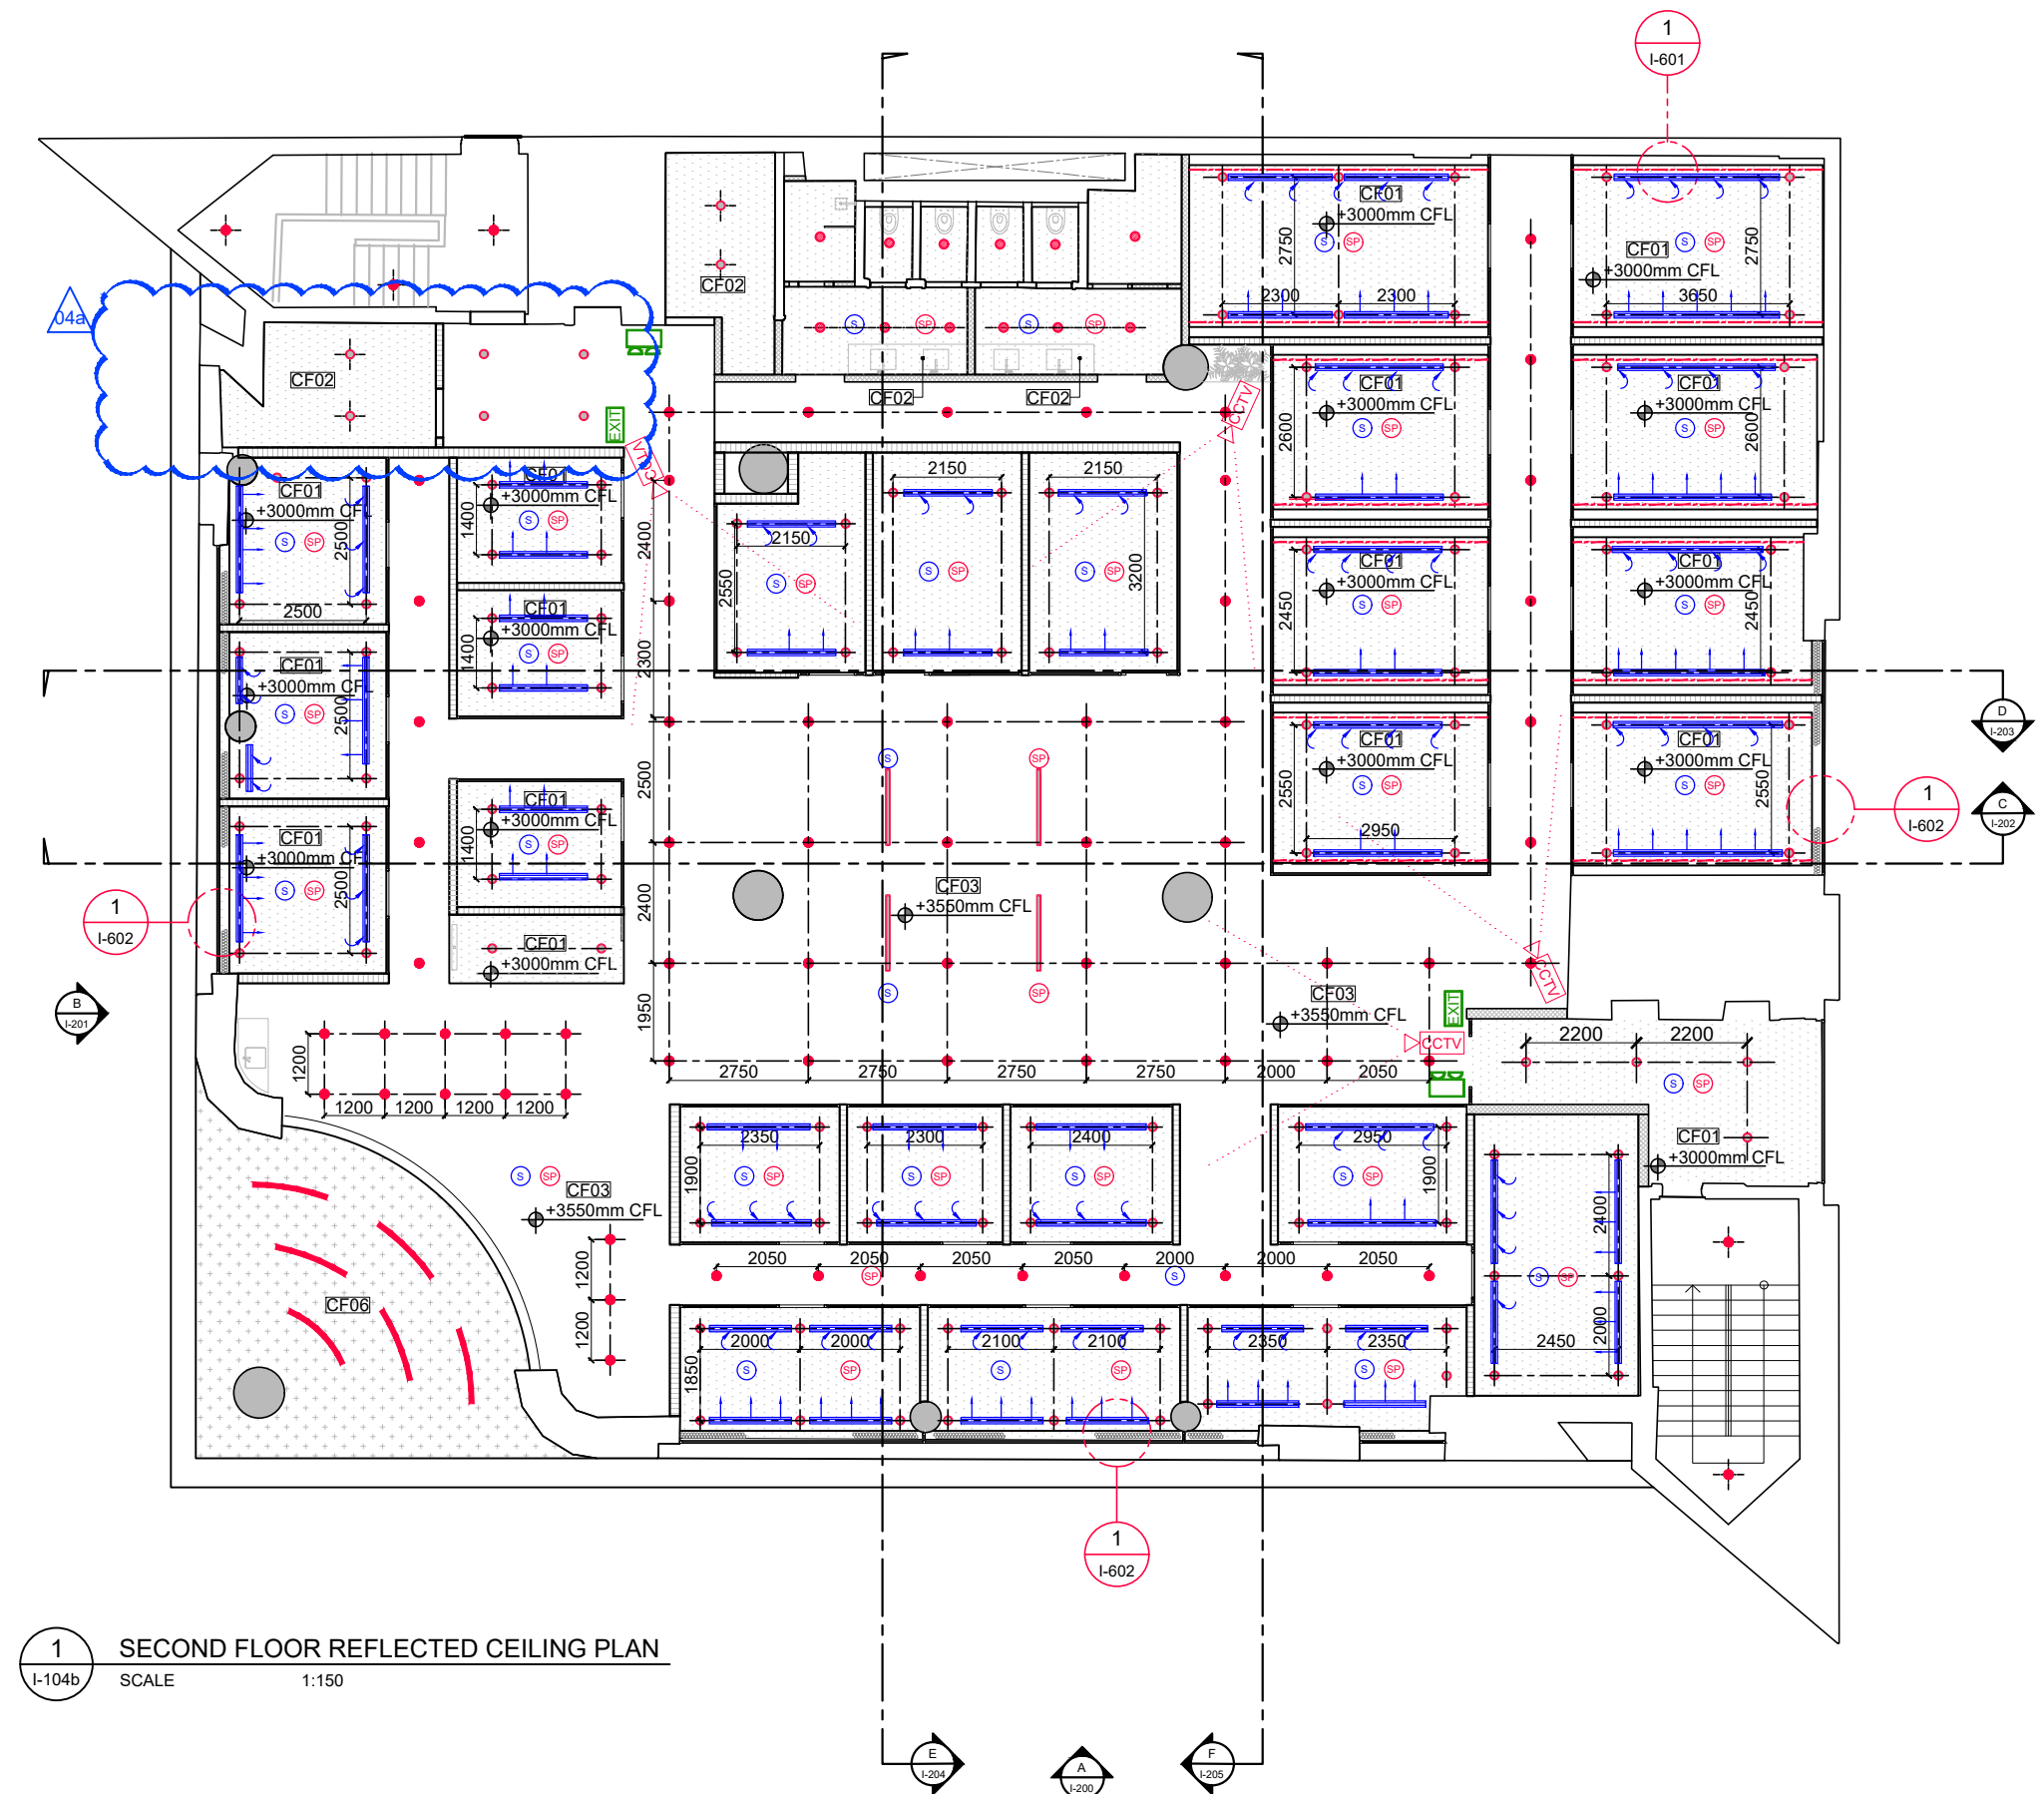

1 SECOND FLOOR REFLECTED CEILING PLAN
I-104b SCALE 1:150

key concept		CONSULTANT	OWNER	PROJECT TITLE	NO.	DESCRIPTION	DATE	SHEET TITLE :		SHEET NO.
				AL HABIB PAVILION HQ	01	TENDER UPDATE	2023.03.22	SECOND FLOOR REFLECTED CEILING PLAN		I-104b
					02	TENDER UPDATE	2023.04.06	SCALE 1:150		
					03	TENDER UPDATE	2023.04.12	DATE: 2023.03.03		
					04	MEETING ROOM CABINET UPDATE	2023.04.25	APPROVED BY: AN	DRAWN BY: AN	
(407A) BLDG. 4, DUBAI DESIGN DISTRICT, DUBAI, UNITED ARAB EMIRATES			ADDRESS: JEDDAH, KSA		04a	TENDER UPDATE	2023.05.05	DESIGNED BY: AN	CHECKED BY: AN	


LEGENDS:	
ELECTRICAL SYMBOLS	
	WATER PROVISION
	DRAINAGE PROVISION
POS	POINT OF SALE
	SINGLE POWER OUTLET
	DOUBLE POWER OUTLET
	3 PHASE POWER OUTLET
	DATA PROVISION
	FLOOR BOX
	FLOOR BOX WITH DATA PROVISION
	CEILING BOX WITH POWER AND DATA PROVISION

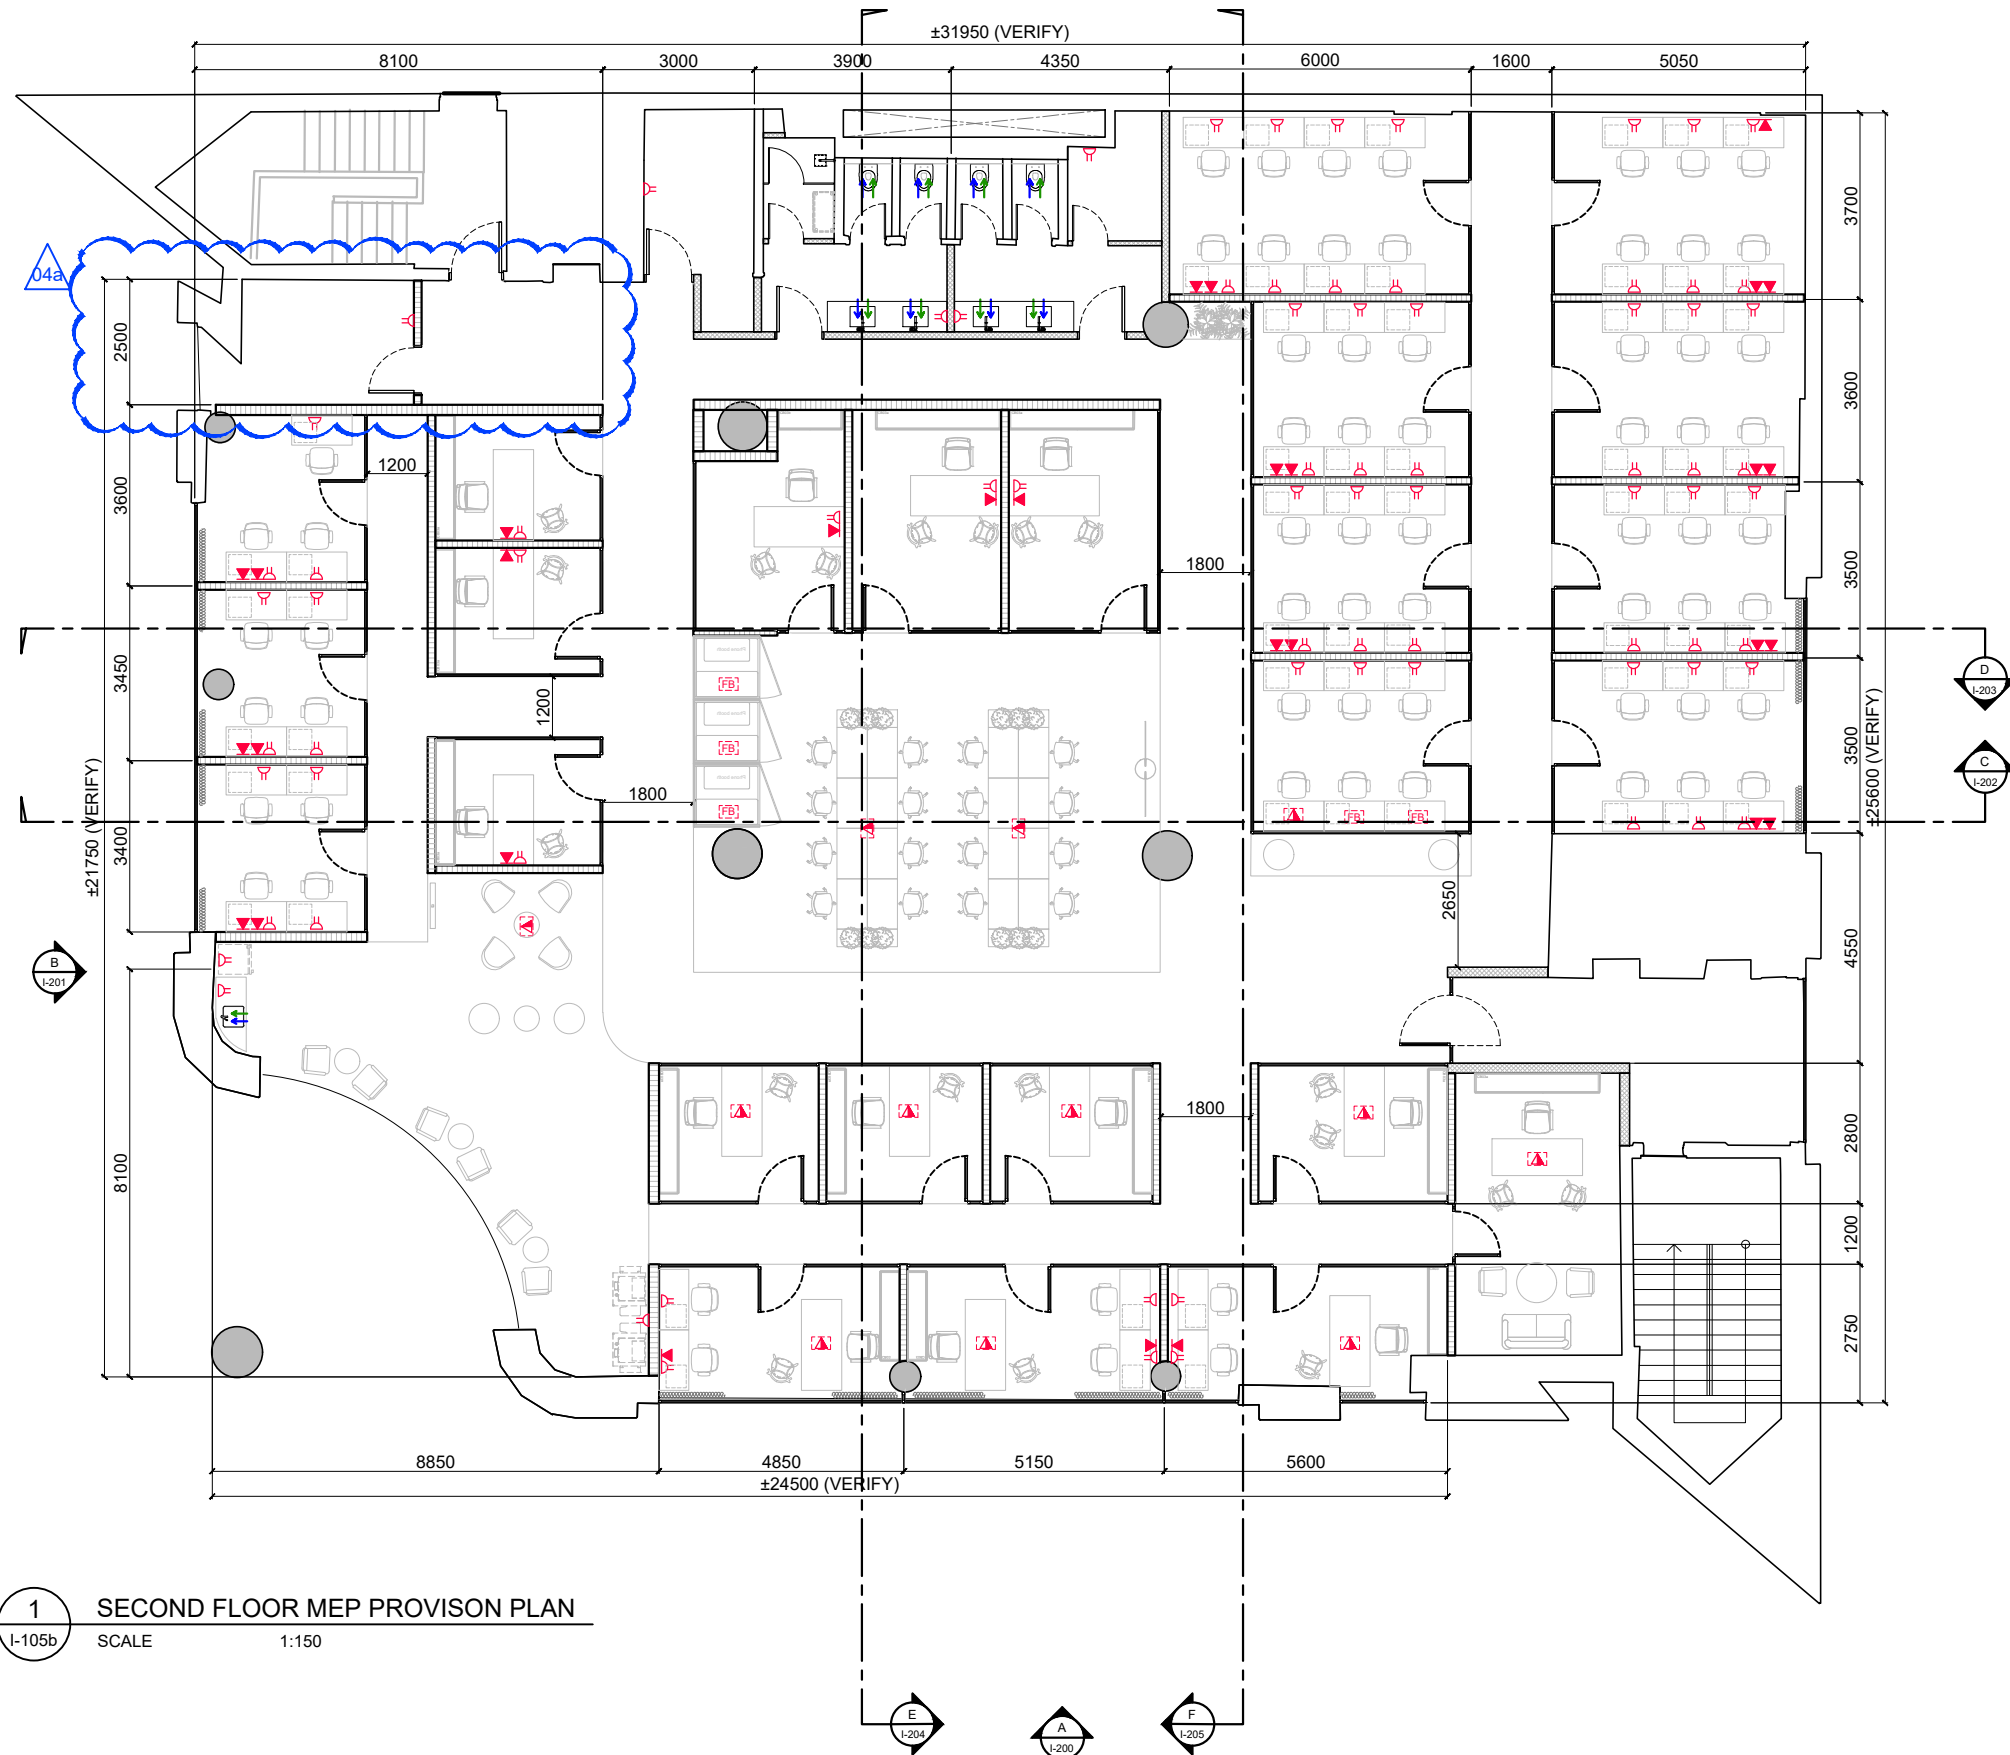

1 SECOND FLOOR MEP PROVISION PLAN
I-105b SCALE 1:150

key concept (407A) BLDG. 4, DUBAI DESIGN DISTRICT, DUBAI, UNITED ARAB EMIRATES		CONSULTANT	OWNER	PROJECT TITLE	NO.	DESCRIPTION	DATE	SHEET TITLE :	SHEET NO.
				AL HABIB PAVILION HQ	01	TENDER UPDATE	2023.03.22	SECOND FLOOR MEP PROVISION PLAN	I-105b
					02	TENDER UPDATE	2023.04.06	SCALE 1:150	
					03	TENDER UPDATE	2023.04.12	DATE: 2023.03.03	
					04	MEETING ROOM CABINET UPDATE	2023.04.25	APPROVED BY: AN DRAWN BY: AN	
			04a	TENDER UPDATE	2023.05.05	DESIGNED BY: AN CHECKED BY: AN			
			ADDRESS: JEDDAH, KSA						

LEGENDS:	
SIGNAGE SYMBOLS	
	30mm THK CUT-OUT "BLACK" ACRYLIC SIGNAGE; BACKLIT WITH POWER OUTLET
	30mm THK CUT-OUT "CREAMY WHITE" ACRYLIC SIGNAGE; FRONTLIT WITH POWER OUTLET
	ARTWORK
	CUT-OUT STICKER SIGNAGE

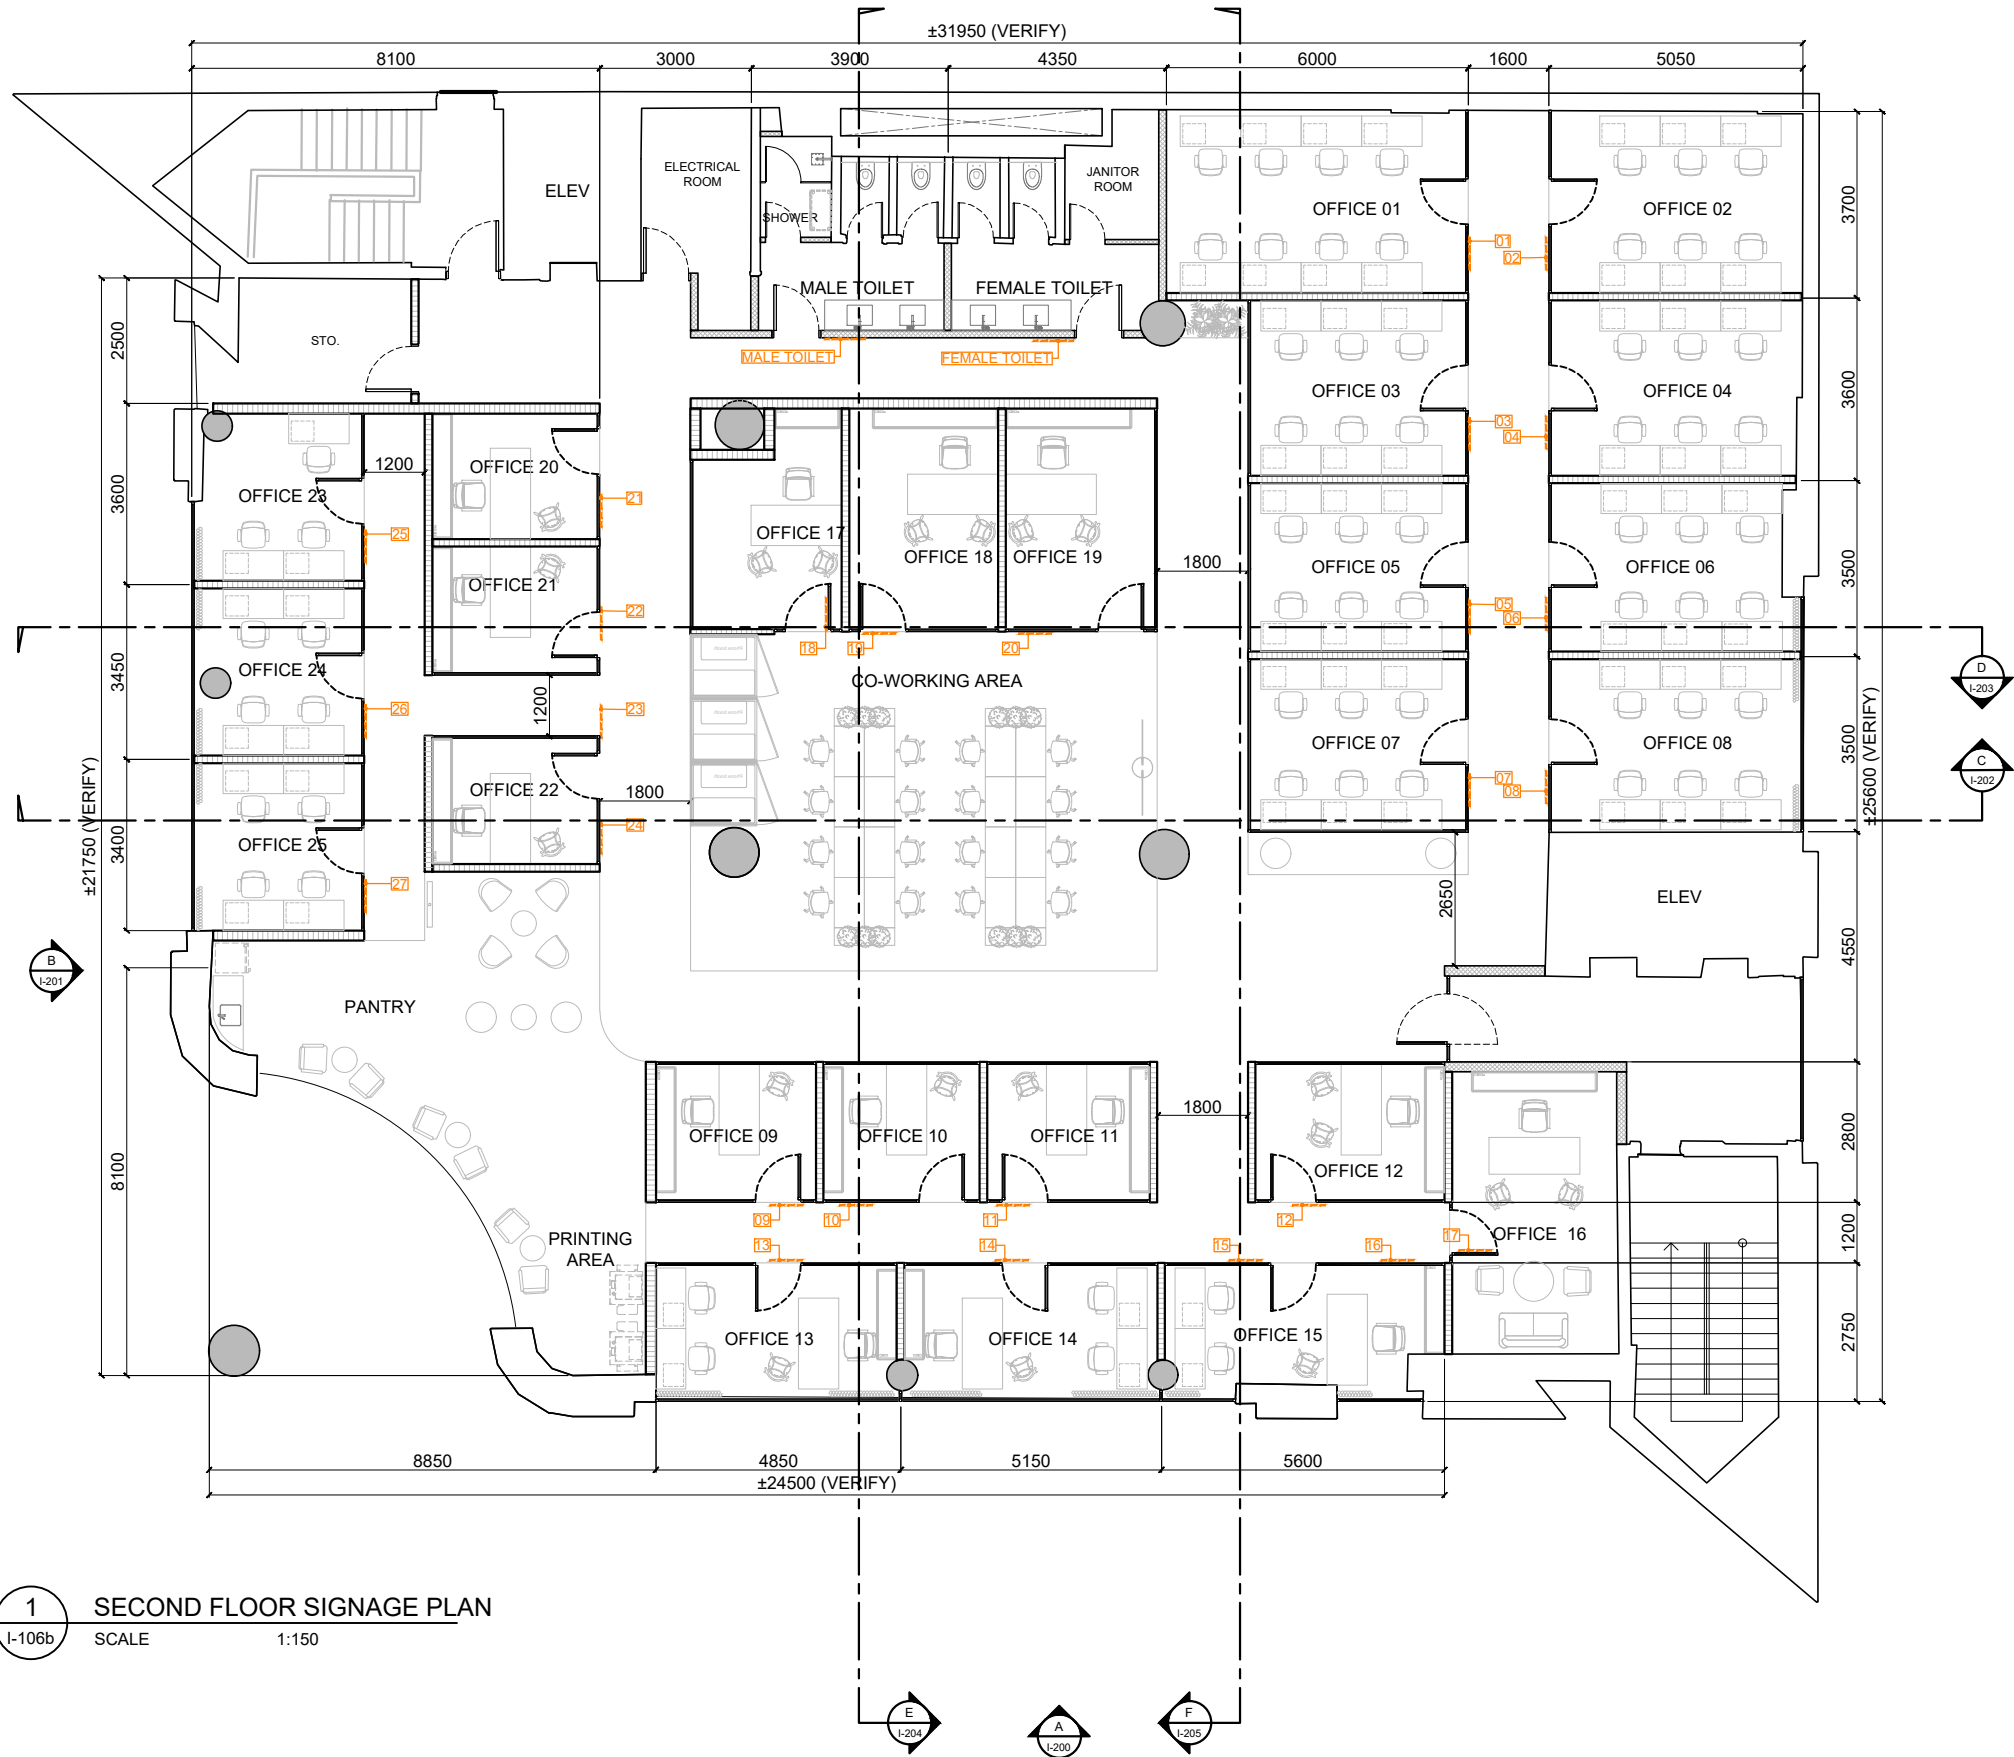

1 SECOND FLOOR SIGNAGE PLAN
I-106b SCALE 1:150

key concept (407A) BLDG. 4, DUBAI DESIGN DISTRICT, DUBAI, UNITED ARAB EMIRATES		CONSULTANT	OWNER	PROJECT TITLE	NO.	DESCRIPTION	DATE	SHEET TITLE :	SHEET NO.
				AL HABIB PAVILION HQ	01	TENDER UPDATE	2023.03.22	SECOND FLOOR SIGNAGE PLAN	I-106b
					02	TENDER UPDATE	2023.04.06	SCALE 1:150	
					03	TENDER UPDATE	2023.04.12	DATE: 2023.03.03	
					04	MEETING ROOM CABINET UPDATE	2023.04.25	APPROVED BY: AN DRAWN BY: AN	
	ADDRESS: JEDDAH, KSA		04a	TENDER UPDATE	2023.05.05	DESIGNED BY: AN CHECKED BY: AN			